

AUTHORITY SEWER MAIN
Ø225mm VC AUTHORITY SEWER
MAIN WITHIN 10M OF BUILDING
FOOTPRINT BASED ON SEWER
SERVICE DIAGRAM AND SEWER
LAYOUT PLAN RECEIVED WHICH
WILL POTENTIALLY REQUIRE OUT OF
SCOPE WORKS. WSC ENGAGEMENT
REQUIRED TO ASSESS AND
CONFIRM WORKS REQUIRED.

2,156 m2 TOTAL GLA
SUB WATER METER
PROVIDE NEW Ø25mm SUB WATER
METER TO SERVE NEW UNIT AND
CONNECT TO EXISTING COLD
WATER PROVISIONS ON SITE.
(77 SPACES)

ON SITE SEWER
NEW UNIT TO CONNECT TO
EXISTING 150mm PVC SEWER MAIN
ON SITE AS PER SEWER LAYOUT
SITE PLAN RECEIVED.
WSC ASSESMENT REQUIRED TO
CONFIRM REQUIREMENTS.

EXISTING UNIT 7

UNDERCROFT
CAR PARKING
SHOWN DASHED
(EXISTING)

AUTHORITY WATER METER
EXISTING 50mm AUTHORITY WATER
METER ASSEMBLY SERVING THE
SITE.

NOTE: THE LOCATION OF PROPERTY ALIGNMENTS IS DETERMINED FROM SURVEY INFORMATION PROVIDED BY SURVEYOR.

DO NOT SCALE THIS DRAWING. VERIFY ALL DIMENSIONS ON SITE BEFORE COMMENCING ANY WORK. COPYRIGHT © THIS DRAWING REMAINS THE PROPERTY OF PACEARCHITECTS. REPRODUCTION IN WHOLE OR PART IS FORBIDDEN.

PACEARCHITECTS
A.B.N. 721 5926 6350
e ppace@pacearchitects.com.au
p 02 9425 1400
m 0404 450 317
w www.pacearchitects.com.au
a Level 1, Suite 5-6, 100 Alexander Street,
Crows Nest, Sydney, NSW 2065

PACE
ARCHITECTS

CLIENT
Hale

PROJECT MANAGER
ENGINE

BUILDER

REVISION	DESCRIPTION	DATE
1	CONCEPT SKETCH REVIEW - UNIT 7A DESIGN UPDATED	11.10.2023
2	ENTRY LOBBY ROTATED 90 DEGREES, GRIDS ADDED, AMENITIES UPDATED	17.10.2023
3	SURVEY ADDED, BUILDING OUTLINE UPDATED	26.10.2023
4	BUILDING HEIGHTS UPDATED FROM SURVEY. DRAFT DEVELOPMENT TABLE	31.10.2023

**PROPOSED INDUSTRIAL
WAREHOUSE & OFFICES**
145-151 ARTHUR STREET,
HOMEBUSH WEST NSW

0 
purpose SKETCH DESIGN
SITE PLAN - ALTERNATE
SCHEME

scale As indicated **A1**
project no 221102
date 21.11.22
PGT 221102 - SK-003



issue

4

DEVELOPMENT SUMMARY

AREA SCHEDULE (GFA)

SITE AREA	32,100 m2
GF WAREHOUSE AREA	1,864 m2
GF LOBBY OFFICE	16 m2
GF DOCK OFFICE	22 m2
L1 OFFICE (excludes stair)	188 m2
TOTAL BUILDING AREA (GFA)	2,090 m2
AWNING AREA 6m (W) x 7.6m (D)	207 m2
TOTAL BUILDING AREA (INC. AWNINGS)	2,297 m2
HEAVY DUTY PAVEMENT	266 m2

CAR PARKING CALCULATION*

WAREHOUSE:	1,864 m2 / 1 space per 55 m2	=33.89
OFFICE: 16+ 22+ 188m2 =	226 m2 / 1 space per 55 m2	=4.10
TOTAL CAR PARKING REQUIRED (FOR EXTENSION)	38	CAR SPACES


TOTAL CAR PARKING PROVIDED

TOTAL CAR PARKING (EXISTING ESTATE) 390+77=	467	CAR SPACES
TOTAL CAR PARKING (AFTER EXTENSION) 467-77=	390	CAR SPACES

TOTAL CAR PARKING REQUIRED

TOTAL CAR PARKING (EXISTING ESTATE) 94+246=	340	CAR SPACES
TOTAL CAR PARKING REQUIRED (FOR EXTENSION)	38	CAR SPACES
TOTAL CAR PARKING REQUIRED (AFTER EXTENSION)	378	CAR SPACES

*GROSS FLOOR AREA MEASURED TO INTERNAL FACE OF WALLS
AND EXCLUDES VOIDS TO STAIRCASES ON LEVEL 1 (TBC)

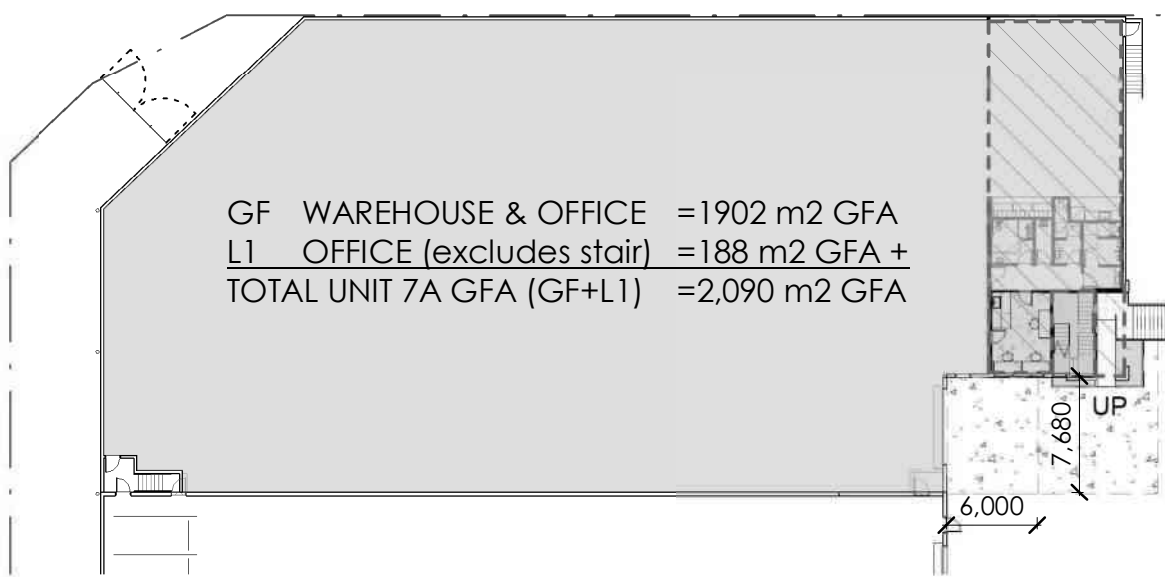

3 GROUND FLOOR
1 : 500 CD-600

Date	03.11.2023	Drawn by	SM	Building Services Engineers ADP consulting Engineers ADP CONSULTING PTY LTD MELBOURNE Level 13 55 Collins St Melbourne VIC 3000 +61 39521 1195 SYDNEY Level 6 33 Eureka St Sydney NSW 2000 +61 28203 5447 BRISBANE Level 10 15 Adelaide St Brisbane QLD 4000 +61 73088 4022 GOLD COAST Level 13 55 Cavill Ave Surfers Paradise QLD 4202 +61 73088 4022 www.adpconsulting.com.au contact@adpconsulting.com.au
Scale	1:100	Checked by	SJ	
Sheet Size	A1	Approved by	SS	
Project Name: 145-151 ARTHUR ST, HOMEBUSH WEST, NSW				
Title: HYDRAULICS SERVICES SPATIALS				
Client: ENGINE ROOM VM				
Job No. SYD2497		Drawing / Sketch No. HY-SK-01		Rev. P1